

PROPOSAL PEMBANGUNAN MENARA MASJID AL IKHLAS



**Desa Meranjat II, Kec. Indralaya Selatan, Kab. Ogan Ilir,
Prov. Sumatera Selatan**

KATA PENGANTAR

Puji syukur kehadiran Allah SWT yang senantiasa melimpahkan rahmat, taufiq, hidayah, serta inayah-Nya kepada kita semua. Shalawat dan salam semoga senantiasa tercurah kepada junjungan kita Nabi Agung Muhammad SAW, beserta keluarga, sahabat, dan umatnya hingga akhir zaman.

Proposal Pembangunan Menara Masjid Al Ikhlas di Desa Meranjat II, Ogan Ilir, Sumatera Selatan ini disusun sebagai bentuk ikhtiar kami dalam mewujudkan sarana peribadatan yang lebih baik dan representatif. Tujuan utama dari pembangunan menara ini adalah untuk memperluas jangkauan gema suara azan, sehingga syiar Islam dapat lebih dirasakan oleh masyarakat di sekitar Meranjat II dan wilayah Ogan Ilir pada umumnya.

Kami menyadari bahwa kelancaran dan kesuksesan pembangunan menara ini sangat bergantung pada doa, dukungan, dan bantuan dana dari para dermawan, instansi pemerintah maupun swasta, serta seluruh lapisan masyarakat.

Oleh karena itu, melalui proposal ini kami mengetuk hati Bapak/Ibu/Saudara/i untuk berkenan menyisihkan sebagian rezekinya sebagai amal jariyah yang pahalanya tidak akan terputus. Atas segala perhatian, dukungan, dan bantuannya untuk Masjid Al Ikhlas, kami ucapkan *Jazakumullah Khairan Katsiran*.

LATAR BELAKANG

Masjid Al Ikhlas merupakan pusat kegiatan ibadah dan keagamaan bagi masyarakat Desa Meranjat II, Ogan Ilir. Seiring dengan bertambahnya jumlah penduduk dan meluasnya permukiman warga di kawasan tersebut, jangkauan suara azan dari masjid ini dirasa belum maksimal dan kurang terdengar hingga ke pelosok

permukiman. Kondisi ini menjadi salah satu hambatan dalam penyiaran panggilan salat lima waktu bagi umat muslim di lingkungan sekitar.

Selain itu, bangunan fisik masjid juga membutuhkan penyempurnaan dari segi arsitektur agar menjadi ikon syiar Islam yang membanggakan bagi warga setempat, khususnya di wilayah Meranjat II. Keberadaan menara masjid tidak hanya berfungsi sebagai tempat meletakkan pengeras suara, tetapi juga sebagai simbol keagungan dan syiar Islam yang terlihat dari kejauhan.

Berangkat dari kondisi dan kebutuhan tersebut, pengurus masjid beserta warga masyarakat Desa Meranjat II sepakat untuk bergotong royong melaksanakan Pembangunan Menara Masjid Al Ikhlas. Pembangunan ini diharapkan dapat menjadi solusi atas keterbatasan jangkauan suara azan sekaligus memperindah estetika bangunan masjid.

NAMA KEGIATAN

Kegiatan ini bernama: Pembangunan Menara Masjid Al Ikhlas, Desa Meranjat II, Kabupaten Ogan Ilir, Sumatera Selatan.

TUJUAN

- Meningkatkan tempat pengeras suara (speaker) sehingga jangkauan suara azan menjadi lebih jauh dan meluas hingga ke seluruh penjuru Desa Meranjat II dan sekitarnya.
- Meningkatkan kualitas syiar agama Islam di wilayah Meranjat II, Kabupaten Ogan Ilir, dan sekitarnya.
- Memperindah estetika dan melengkapi fasilitas fisik Masjid Al Ikhlas agar menjadi ikon kebanggaan dan sarana ibadah yang lebih representatif bagi masyarakat setempat.

SASARAN & MANFAAT

Sasaran:

- Terbangunnya 1 (satu) unit Menara Masjid dengan tinggi [Tinggi Menara] meter di Masjid Al Ikhlas, Desa Meranjat II.

Manfaat:

- Memudahkan warga muslim di sekitar untuk mengetahui masuknya waktu salat fardu secara tepat waktu.
- Menumbuhkan rasa kebersamaan, gotong royong, dan kepedulian sosial antar warga selama masa pembangunan menara di lingkungan Desa Meranjat II.

RENCANA WAKTU & LOKASI

- **Waktu Pelaksanaan:** Pengerjaan menara ditargetkan dalam waktu kurang lebih 6 bulan (sejak awal dimulai hingga selesai)
- **Lokasi Pembangunan:** Area Masjid Al Ikhlas, Desa Meranjat II, Kecamatan Indralaya Selatan, Kabupaten Ogan Ilir, Sumatera Selatan.

RANCANGAN ANGGARAN BIAYA

Adapun total perkiraan biaya yang dibutuhkan untuk pelaksanaan Pembangunan Menara Masjid Al Ikhlas sebagai berikut:

No.	JENIS PEKERJAAN	VOLUME	SAT	HARGA SATUAN (Rp.)		JUMLAH HARGA (Rp.)		TOTAL (Rp.)
				BAHAN	UPAH	BAHAN	UPAH	
I	PEKERJAAN PERSIAPAN							
1	Pembersihan Lapangan + Direksi Keet	36,00	M²		16.012,50	-	576.450,00	576.450,00
2	Pengukuran & Pemasangan Bowplank	24,00	M'		25.095,00	-	602.280,00	602.280,00
	- Kayu 5/7	0,288	M³	3.969.000,00		1.143.072,00	-	1.143.072,00
	- Paku biasa 2" - 5"	0,480	Kg	17.692,50		8.492,40	-	8.492,40
	- Kayu papan 3/20	0,168	M³	3.969.000,00		666.792,00	-	666.792,00
	Sub Total I							2.997.086,40
II	PEKERJAAN TANAH							
1	Penggalian Tanah Pondasi	60,75	M³		120.000,00	-	7.290.000,00	7.290.000,00
2	Timbunan Urugan Tanah	60,75	M³		33.390,00	-	2.028.442,50	2.028.442,50
	- Tanah Urug	60,75	M³	106.785,00		6.487.188,75	-	6.487.188,75
3	Urugan Pasir Dibawah Keramik T = 10 CM	0,97	M³		33.390,00	-	32.295,14	32.295,14
	- Pasir Urug	1,16	M³	160.000,00		185.704,32	-	185.704,32
4	Pengeboran Trucuan	40,00	Bh		20.000,00	-	800.000,00	800.000,00
	- Bambu/Kayu Dolken	40,00	Bh	135.000,00		5.400.000,00	-	5.400.000,00
	Sub Total II							22.223.630,71

III	PEKERJAAN PONDASI							
1	Footplat Uk. 150 x 150 x 30 cm							
	Pembesian Pondasi	206,00	Kg		5.000,00		1.030.000,00	1.030.000,00
	- Besi D13	200,00	Kg	15.000,00		3.000.000,00	-	3.000.000,00
	- Kawat Bendrat	6,00	Kg	26.250,00		157.500,00	-	157.500,00
	Bekisting Pondasi	7,20	M²		41.265,00	-	297.108,00	297.108,00
	- Kayu Sembarang	0,29	M³	6.069.000,00		1.747.872,00	-	1.747.872,00
	- Paku Biasa 2" - 5"	0,72	Kg	17.692,50		12.738,60	-	12.738,60
	- Minyak Bekisting	0,72	Ltr	16.000,00		11.520,00	-	11.520,00
	Cor Beton Pondasi mutu K-250	2,70	M³		225.000,00	-	607.500,00	607.500,00
	- Semen portland	1.036,80	Kg	3.625,13		3.758.529,60	-	3.758.529,60
	- Pasir pasang	2,08	M³	139.650,00		290.192,84	-	290.192,84
	- Batu Kerikil (2-3cm)	2,19	M³	325.000,00		710.775,00	-	710.775,00
	Urugan Pasir Dibawah Pondasi T = 5 cm	2,03	M³		33.390,00		67.614,75	67.614,75
	- Pasir Urug	2,43	M³	125.000,00		303.750,00	-	303.750,00
	Lantai Kerja 1 : 3 : 5 Dibawah Pondasi T = 5 cm	2,03	M³		33.390,00	-	67.614,75	67.614,75
	- Semen portland	20,25	Kg	3.625,13		73.408,78	-	73.408,78
	- Pasir pasang	0,61	M³	150.000,00		91.125,00	-	91.125,00
	- Batu Kerikil (2-3cm)	1,42	M³	221.025,00		313.302,94	-	313.302,94
2	Kolom Pedestal Uk. 30 x 30 cm							

	Pembesian Kolom Pedestal	558,24	Kg		1.071,00	-	597.879,15	597.879,15
	- Besi D13	398,75	Kg	15.000,00		5.981.184,00	-	5.981.184,00
	- Besi Ø8	159,50	Kg	5.512,50		879.234,05	-	879.234,05
	- Kawat Bendrat	8,37	Kg	26.250,00		219.808,51	-	219.808,51
	Bekisting Kolom Pedestal	16,80	M²		72.765,00	-	1.222.452,00	1.222.452,00
	- Kayu Sembarang	0,67	M³	6.069.000,00		4.078.368,00	-	4.078.368,00
	- Paku Biasa 2" - 5"	6,72	Kg	21.892,50		147.117,60	-	147.117,60
	- Minyak Bekisting	3,36	Ltr	16.000,00		53.760,00	-	53.760,00
	- Balok Kayu Sembarang	0,25	M³	6.069.000,00		1.529.388,00	-	1.529.388,00
	- Triplek Tebal 9 mm	5,88	Lbr	236.775,00		1.392.237,00	-	1.392.237,00
	- Kayu Dolken dia. 4"	33,60	Btg	28.350,00		952.560,00	-	952.560,00
	Cor Beton Kolom Pedestal mutu K-250	1,23	M³		222.180,00	-	273.014,78	273.014,78
	- Semen portland	471,86	Kg	3.625,13		1.710.548,58	-	1.710.548,58
	- Pasir pasang	0,95	M³	160.650,00		151.930,13	-	151.930,13
	- Batu Kerikil (2-3cm)	1,00	M³	326.025,00		324.501,81	-	324.501,81
3	Sloof Uk. 20 x 40 cm							
	Pembesian Sloof	508,82	Kg		1.071,00	-	544.941,94	544.941,94
	- Besi D13	363,44	Kg	15.000,00		5.451.600,00	-	5.451.600,00
	- Besi Ø8	145,38	Kg	5.512,50		801.385,20	-	801.385,20
	- Kawat Bendrat	7,63	Kg	26.250,00		200.346,30	-	200.346,30
	Bekisting Sloof	11,20	M²		72.765,00	-	814.968,00	814.968,00

	- Kayu Sembarang	0,45	M³	6.069.000,00		2.718.912,00	-	2.718.912,00
	- Paku Biasa 2" - 5"	4,48	Kg	17.692,50		79.262,40	-	79.262,40
	- Minyak Bekisting	2,24	Ltr	16.000,00		35.840,00	-	35.840,00
	Cor Beton Sloof mutu K-250	1,12	M³		222.180,00	-	248.841,60	248.841,60
	- Semen portland	430,08	Kg	3.625,13		1.559.093,76	-	1.559.093,76
	- Pasir pasang	0,86	M³	139.650,00		120.376,29	-	120.376,29
	- Batu Kerikil (2-3cm)	0,91	M³	221.025,00		200.513,88	-	200.513,88
4	Pasangan Rollag Bata	5,60	M²		53.025,00	-	296.940,00	296.940,00
	- Bata merah	560,00	Bh	577,50		323.400,00	-	323.400,00
	- Semen portland	155,01	Kg	3.625,13		561.923,38	-	561.923,38
	- Pasir pasang	0,25	M³	116.182,50		29.277,99	-	29.277,99
	Sub Total III							46.042.158,61
IV	PEKERJAAN BETON							
1	Rabat Beton T = 12 cm							
	Cor Rabat Beton 1 Pc : 2 Ps : 3 Kr	1,47	M³		121.275,00	-	178.274,25	178.274,25
	- Semen portland	289,59	Kg	3.625,13		1.049.799,95	-	1.049.799,95
	- Pasir pasang	0,69	M³	178.500,00		123.325,65	-	123.325,65
	- Batu Kerikil (2-3cm)	1,38	M³	326.025,00		450.501,35	-	450.501,35
2	Kolom Struktur Uk. 30 x 30 cm							
	Pembesian Kolom Struktur	1.153,70	Kg		1.071,00	-	1.235.616,92	1.235.616,92
	- Besi D13	824,07	Kg	15.000,00		12.361.113,60	-	12.361.113,60

	- Besi Ø8	329,63	Kg	5.512,50		1.817.083,70	-	1.817.083,70
	- Kawat Bendrat	17,31	Kg	26.250,00		454.270,92	-	454.270,92
	Bekisting Kolom Struktur	39,68	M²		72.765,00	-	2.887.315,20	2.887.315,20
	- Kayu Sembarang	1,59	M³	6.069.000,00		9.632.716,80	-	9.632.716,80
	- Paku Biasa 2" - 5"	15,87	Kg	17.692,50		280.815,36	-	280.815,36
	- Minyak Bekisting	7,94	Ltr	16.000,00		126.976,00	-	126.976,00
	- Balok Kayu Sembarang	0,60	M³	6.069.000,00		3.612.268,80	-	3.612.268,80
	- Triplek Tebal 9 mm	13,89	Lbr	236.775,00		3.288.331,20	-	3.288.331,20
	- Kayu Dolken dia. 4"	79,36	Btg	21.000,00		1.666.560,00	-	1.666.560,00
	Cor Beton Kolom Struktur mutu K-250	2,54	M³		222.180,00	-	564.230,55	564.230,55
	- Semen portland	975,18	Kg	3.625,13		3.535.133,74		3.535.133,74
	- Pasir pasang	1,95	M³	178.500,00		348.876,60		348.876,60
	- Batu Kerikil (2-3cm)	2,06	M³	326.025,00		670.637,08		670.637,08
3	Balok Latei Uk. 11 x 30 cm							
	Pembesian Balok Latei	145,21	Kg		1.071,00	-	155.516,27	155.516,27
	- Besi D13	103,72	Kg	15.000,00		1.555.785,00	-	1.555.785,00
	- Besi Ø8	41,49	Kg	5.512,50		228.700,40	-	228.700,40
	- Kawat Bendrat	2,18	Kg	26.250,00		57.175,10	-	57.175,10
	Bekisting Balok Latei	12,74	M²		72.765,00	-	927.026,10	927.026,10
	- Kayu Sembarang	0,51	M³	6.069.000,00		3.092.762,40	-	3.092.762,40
	- Paku Biasa 2" - 5"	5,10	Kg	17.692,50		90.160,98	-	90.160,98

	- Minyak Bekisting	2,55	Ltr	16.000,00		40.768,00	-	40.768,00
	- Balok Kayu Sembarang	0,19	M³	6.069.000,00		1.159.785,90	-	1.159.785,90
	- Triplek Tebal 9 mm	4,46	Lbr	236.775,00		1.055.779,73	-	1.055.779,73
	- Kayu Dolken dia. 4"	25,48	Btg	21.000,00		535.080,00	-	535.080,00
	Cor Beton Balok Latei mutu K-250	0,46	M³		222.180,00	-	102.647,16	102.647,16
	- Semen portland	177,41	Kg	3.625,13		643.126,18	-	643.126,18
	- Pasir pasang	0,36	M³	139.650,00		49.655,22	-	49.655,22
	- Batu Kerikil (2-3cm)	0,37	M³	221.025,00		82.711,98	-	82.711,98
4	Balok Dak Beton Uk. 20 x 40 cm							
	Pembesian Balok Dak Beton	1.017,63	Kg		1.071,00	-	1.089.883,87	1.089.883,87
	- Besi D13	726,88	Kg	15.000,00		10.903.200,00	-	10.903.200,00
	- Besi Ø8	290,75	Kg	5.512,50		1.602.770,40	-	1.602.770,40
	- Kawat Bendrat	15,26	Kg	26.250,00		400.692,60	-	400.692,60
	Bekisting Balok Dak Beton	33,60	M²		72.765,00	-	2.444.904,00	2.444.904,00
	- Kayu Sembarang	1,34	M³	6.069.000,00		8.156.736,00	-	8.156.736,00
	- Paku Biasa 2" - 5"	13,44	Kg	17.692,50		237.787,20	-	237.787,20
	- Minyak Bekisting	6,72	Ltr	16.000,00		107.520,00	-	107.520,00
	- Balok Kayu Sembarang	0,50	M³	6.069.000,00		3.058.776,00	-	3.058.776,00
	- Triplek Tebal 9 mm	11,76	Lbr	236.775,00		2.784.474,00	-	2.784.474,00
	- Kayu Dolken dia. 4"	67,20	Btg	21.000,00		1.411.200,00	-	1.411.200,00
	Cor Beton Balok Dak Beton	2,24	M³		222.180,00	-	497.683,20	497.683,20

	- Semen portland	860,16	Kg	3.625,13		3.118.187,52	-	3.118.187,52
	- Pasir pasang	1,72	M³	139.650,00		240.752,58	-	240.752,58
	- Batu Kerikil (2-3cm)	1,81	M³	221.025,00		401.027,76	-	401.027,76
5	Dak Beton T = 12 cm							
	Pembesian Dag Beton	183,02	Kg		1.071,00	-	196.009,07	196.009,07
	- Besi Ø10	183,02	Kg	5.512,50		1.008.870,19	-	1.008.870,19
	- Kawat Bendrat	2,75	Kg	26.250,00		72.062,16	-	72.062,16
	Bekisting Dak Beton	12,25	M²		52.080,00	-	637.980,00	637.980,00
	- Kayu Sembarang	0,49	M³	6.069.000,00		2.973.810,00	-	2.973.810,00
	- Paku Biasa 2" - 5"	4,90	Kg	17.692,50		86.693,25	-	86.693,25
	- Minyak Bekisting	2,45	Ltr	16.000,00		39.200,00	-	39.200,00
	- Balok Kayu Sembarang	0,18	M³	6.069.000,00		1.115.178,75	-	1.115.178,75
	- Triplek Tebal 9 mm	4,29	Lbr	236.775,00		1.015.172,81	-	1.015.172,81
	- Kayu Dolken dia. 4"	73,50	Btg	21.000,00		1.543.500,00	-	1.543.500,00
	Cor Dak Beton Elev. 2 mutu K-250	1,47	M³		222.180,00	-	326.604,60	326.604,60
	- Semen portland	564,48	Kg	3.625,13		2.046.310,56	-	2.046.310,56
	- Pasir pasang	1,13	M³	139.650,00		157.993,88	-	157.993,88
	- Batu Kerikil (2-3cm)	1,19	M³	221.025,00		263.174,47	-	263.174,47
	Sub Total IV							101.998.682,92
V	PEKERJAAN DINDING, KUSEN, LANTAI DAN ORNAMEN GRC							
1	Pasangan Dinding Tebal 1/2 Bata 1 : 5 Diatas Elev. +/- 0.00	84,00	M²		38.325,00	-	3.219.300,00	3.219.300,00

	- Bata merah	5.880,00	Bh	577,50		3.395.700,00	-	3.395.700,00
	- Semen portland	813,12	Kg	3.625,13		2.947.661,64	-	2.947.661,64
	- Pasir pasang	3,78	M³	95.182,50		359.789,85	-	359.789,85
2	Plesteran Dinding 1 : 5 Tebal 15 mm	168,00	M²		64.575,00	-	10.848.600,00	10.848.600,00
	- Semen portland	870,91	Kg	3.625,13		3.157.164,86	-	3.157.164,86
	- Pasir pasang	4,37	M³	95.182,50		415.757,16	-	415.757,16
3	Keramik Lantai	25,00	M²		43.575,00	-	1.089.375,00	1.089.375,00
	- Keramik lantai	25,00	M²	126.000,00		3.150.000,00	-	3.150.000,00
	- Semen portland	250,00	Kg	3.625,13		906.281,25	-	906.281,25
	- Pasir pasang	12,50	M³	95.182,50		1.189.781,25	-	1.189.781,25
4	Ornamen Kusen							
	- Kusen Pintu 90 x 230 cm	1,00	Bh	3.500.000,00		3.500.000,00	-	3.500.000,00
5	Ornamen Ornamen GRC	41,28	M²		200.000,00		8.256.000,00	8.256.000,00
	- Ornamen GRC Masif	41,28	M²	700.000,00		28.896.000,00	-	28.896.000,00
	Sub Total V							71.331.411,01
VI	PEKERJAAN LISTRIK DAN SANITASI							
1	Intalasi listrik	1,00	-		1.500.000,00	-	1.500.000,00	1.500.000,00
	- Instalasi listrik menara beton	1,00	-	750.000,00		750.000,00		750.000,00
	- Instalasi listrik menara GRC	1,00	-	12.500.000,00		12.500.000,00		12.500.000,00
2	Instalasi Penangkal Petir	1,00	-		3.000.000,00	-	3.000.000,00	3.000.000,00

	- Penangkal petir menara GRC	1,00	-	5.000.000,00		5.000.000,00		5.000.000,00
	Sub Total VI							22.750.000,00
VII	PEKERJAAN MENARA GRC							
1	Menara GRC Diameter 2,4 m Tinggi 17 m	128,11	M ²	1.150.000,00	350.000,00	147.328.800,00	44.839.200,00	192.168.000,00
	Sub Total VII							192.168.000,00

No.	JENIS PEKERJAAN	JUMLAH HARGA (Rp.)
I	PEKERJAAN PERSIAPAN	Rp 2.997.086,40
II	PEKERJAAN TANAH	Rp 22.223.630,71
III	PEKERJAAN PONDASI	Rp 46.042.158,61
IV	PEKERJAAN BETON	Rp 101.998.682,92
V	PEKERJAAN DINDING, KUSEN, LANTAI DAN ORNAMEN GRC	Rp 71.331.411,01
VI	PEKERJAAN LISTRIK DAN SANITASI	Rp 22.750.000,00
VII	PEKERJAAN MENARA GRC	Rp 192.168.000,00
JUMLAH		Rp 459.510.969,66
DIBULATKAN		Rp 459.510.000,00
TERBILANG :		Empat Ratus Lima Puluh Sembilan Juta Lima Ratus Sepuluh Ribu Rupiah

PENUTUP

Demikian proposal ini kami sampaikan sebagai gambaran umum tentang rencana Pembangunan Menara Masjid Al Ikhlas di Desa Meranjat II. Kami sangat mengharapkan doa restu serta partisipasi aktif dari Bapak/Ibu/Saudara/i sekalian agar niat baik ini dapat terlaksana dengan lancar tanpa suatu halangan apapun.

Semoga setiap bantuan yang diberikan, baik berupa moril maupun materiil, senantiasa dicatat sebagai amal ibadah di sisi Allah SWT dan dibalas dengan rezeki yang berlipat ganda. Amin Ya Rabbal 'Alamin.

Atas perhatian dan kerja sama yang baik, kami haturkan terima kasih.

L

A

M

P

I

R

A

N




GUBUG IMAJINASI

Desa Undaan Kidul Gg. 5 RT. 02/02
Kec. Undaan - Kab. Kudus 59372
Jawa Tengah (085727292338)

Konsep Desain :

MENARA MASJID
L. 3 T. 23 METER

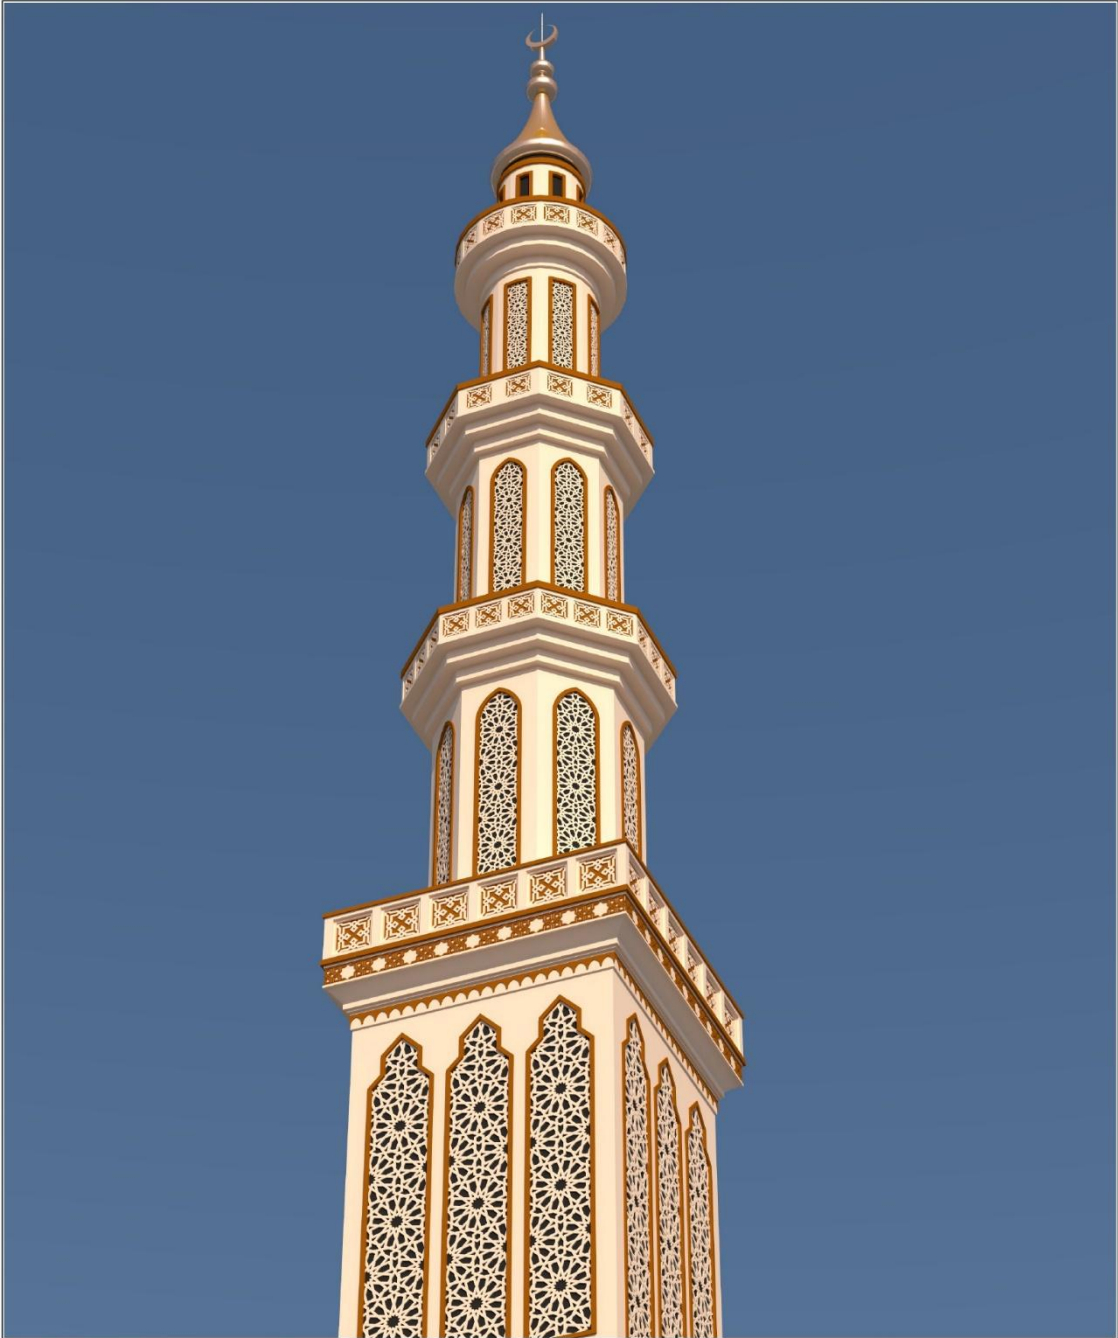

PERSPEKTIF 1

Skala NTS

	Nama Proyek	Pemilik Proyek	Nama Gambar	Skala	Digambar Oleh	Ttd	Tanggal
	MENARA MASJID L. 3 T. 23 METER	-	Perspektif 1	NTS	GUBUG IMAJINASI 085727292338		30 June 2026
	Lokasi Proyek	Catatan			Disetujui Oleh	Ttd	No Lembar
	-	-					01 A3




PERSPEKTIF 2
Skala NTS

	Nama Proyek	Pemilik Proyek	Nama Gambar	Skala	Digambar Oleh	Ttd	Tanggal
	MENARA MASJID L. 3 T. 23 METER	-	Perspektif 2	NTS	GUBUG IMAJINASI 085727292338		30 June 2026
	Lokasi Proyek	Catatan			Disetujui Oleh	Ttd	No Lembar Ukuran Kertas
	-	-					02 A3




PERSPEKTIF 3
Skala NTS


	Nama Proyek	Pemilik Proyek	Nama Gambar	Skala	Digambar Oleh	Ttd	Tanggal
	MENARA MASJID L. 3 T. 23 METER	-	Perspektif 3	NTS	GUBUG IMAJINASI 085727292338		30 June 2026
	Lokasi Proyek	Catatan			Disetujui Oleh	Ttd	No Lembar
	-	-					03
							A3

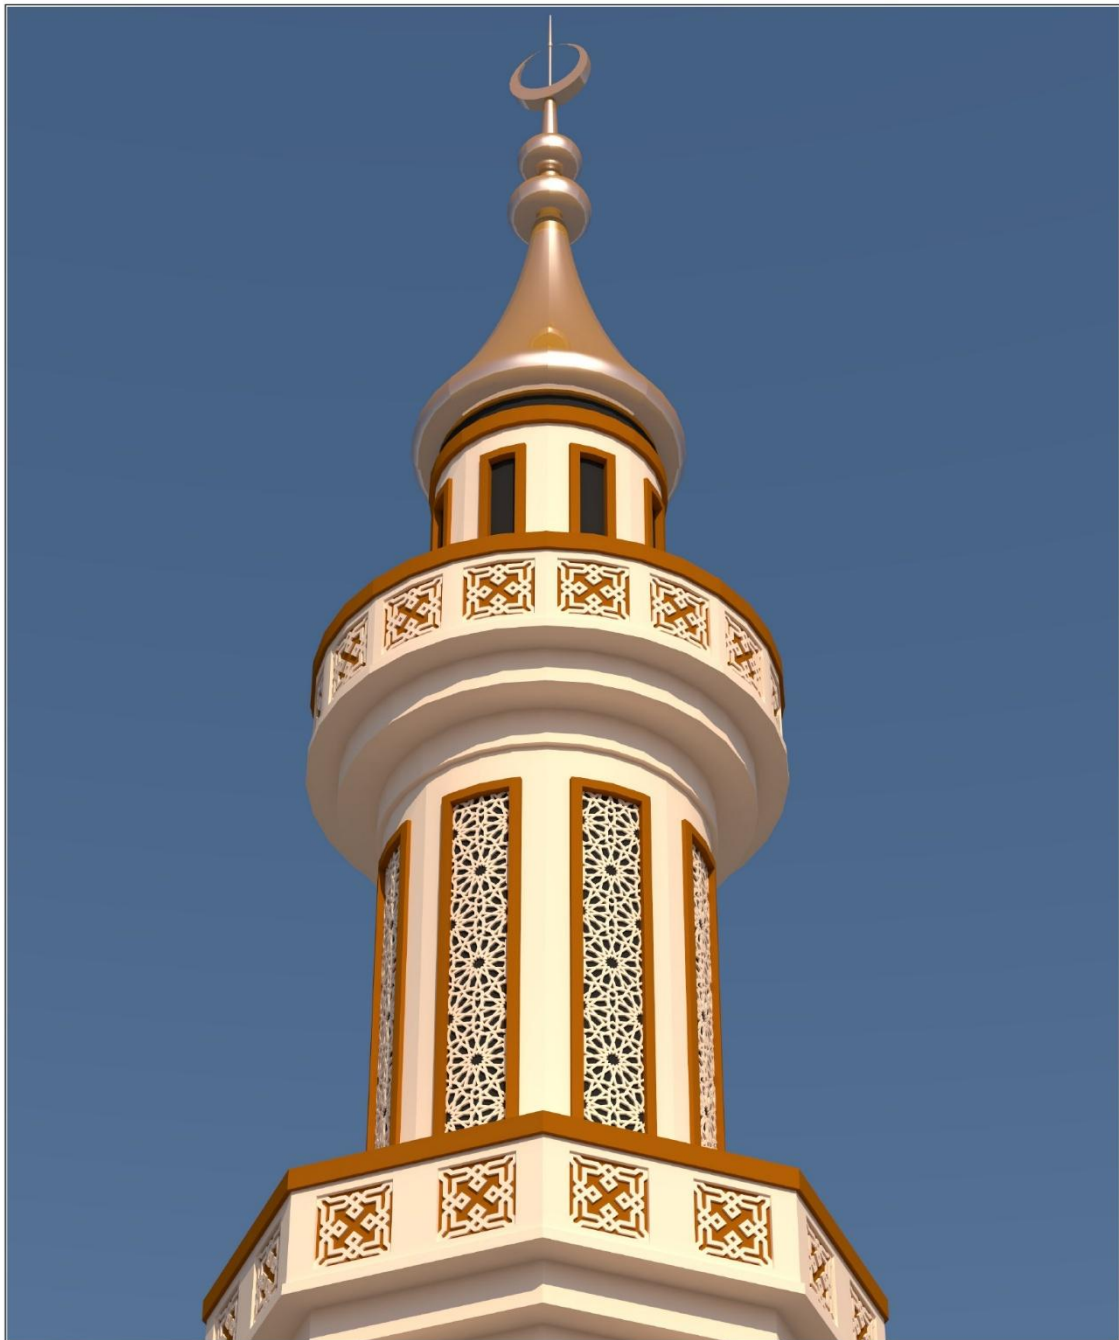

PERSPEKTIF 4
Skala NTS

	Nama Proyek	Pemilik Proyek	Nama Gambar	Skala	Digambar Oleh	Ttd	Tanggal
	MENARA MASJID L. 3 T. 23 METER	-	Perspektif 4	NTS	GUBUG IMAJINASI 085727292338		30 June 2026
	Lokasi Proyek	Catatan			Disetujui Oleh	Ttd	No Lembar
	-	-					04
							A3

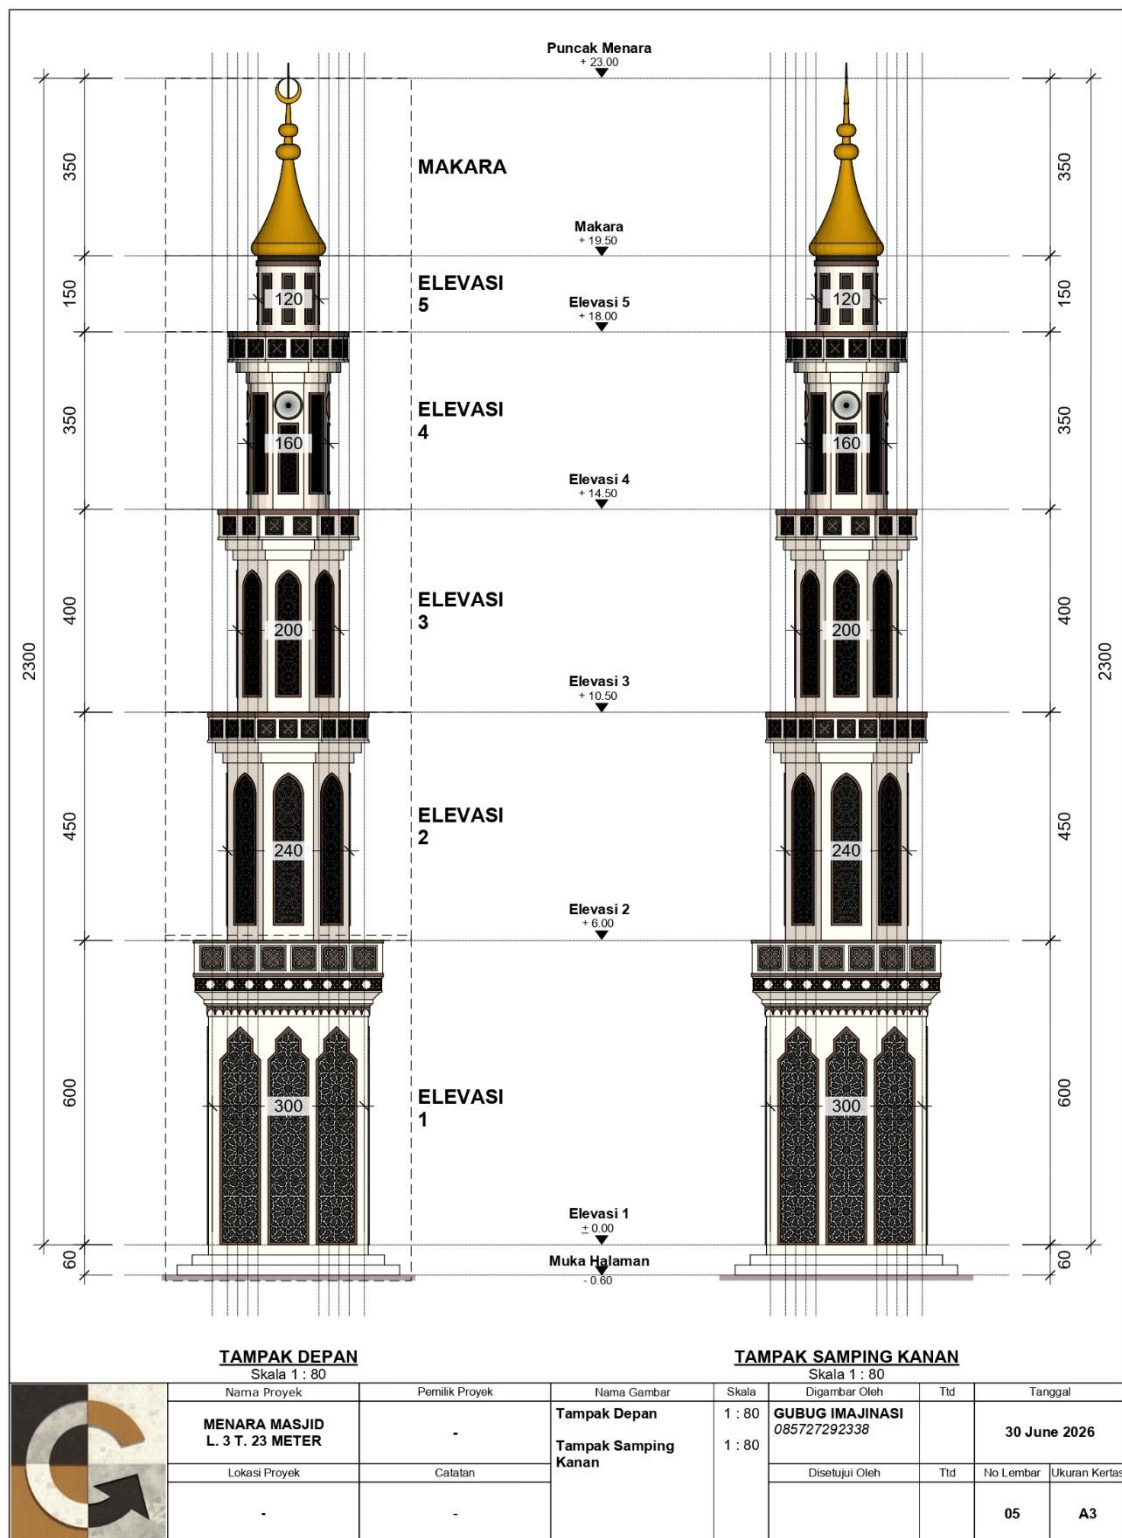


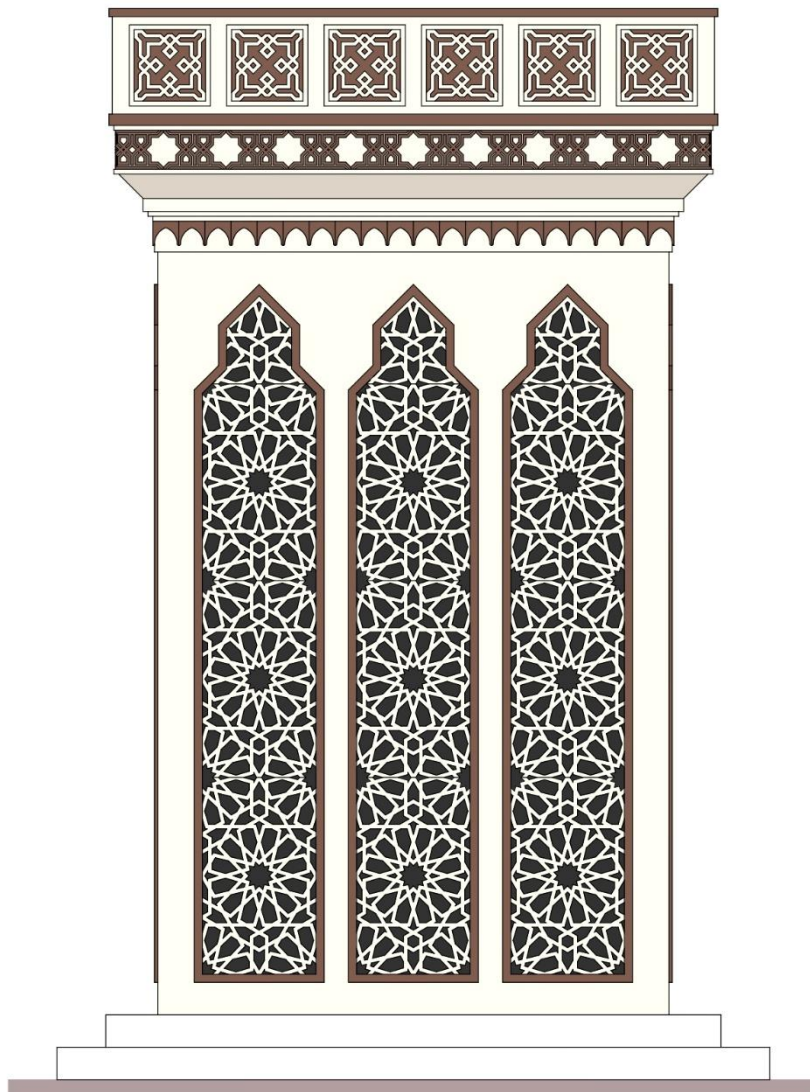

DETAIL ELEVASI 1

Skala 1 : 25


	Nama Proyek	Pemilik Proyek	Nama Gambar	Skala	Digambar Oleh	Ttd	Tanggal
	MENARA MASJID L. 3 T. 23 METER	-	Detail Elevasi 1	1 : 25	GUBUG IMAJINASI 085727292338		30 June 2026
	Lokasi Proyek	Catatan			Disetujui Oleh	Ttd	No Lembar
	-	-					06
							A3

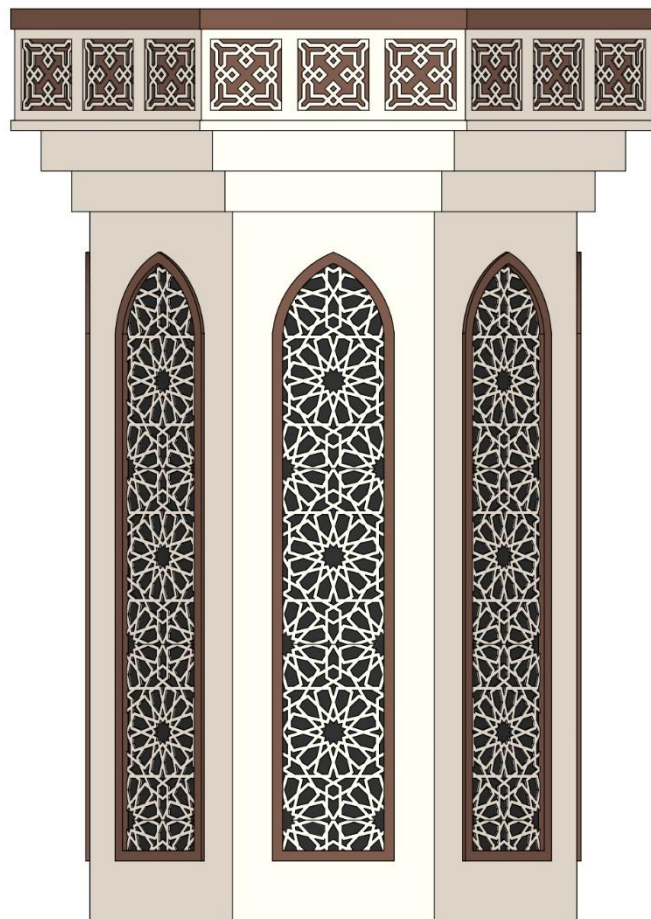

DETAIL ELEVASI 2

Skala 1 : 20


	Nama Proyek	Pemilik Proyek	Nama Gambar	Skala	Digambar Oleh	Ttd	Tanggal
	MENARA MASJID L. 3 T. 23 METER	-	Detail Elevasi 2	1 : 20	GUBUG IMAJINASI 085727292338		30 June 2026
	Lokasi Proyek	Catatan			Disetujui Oleh	Ttd	No Lembar
	-	-					07
							A3

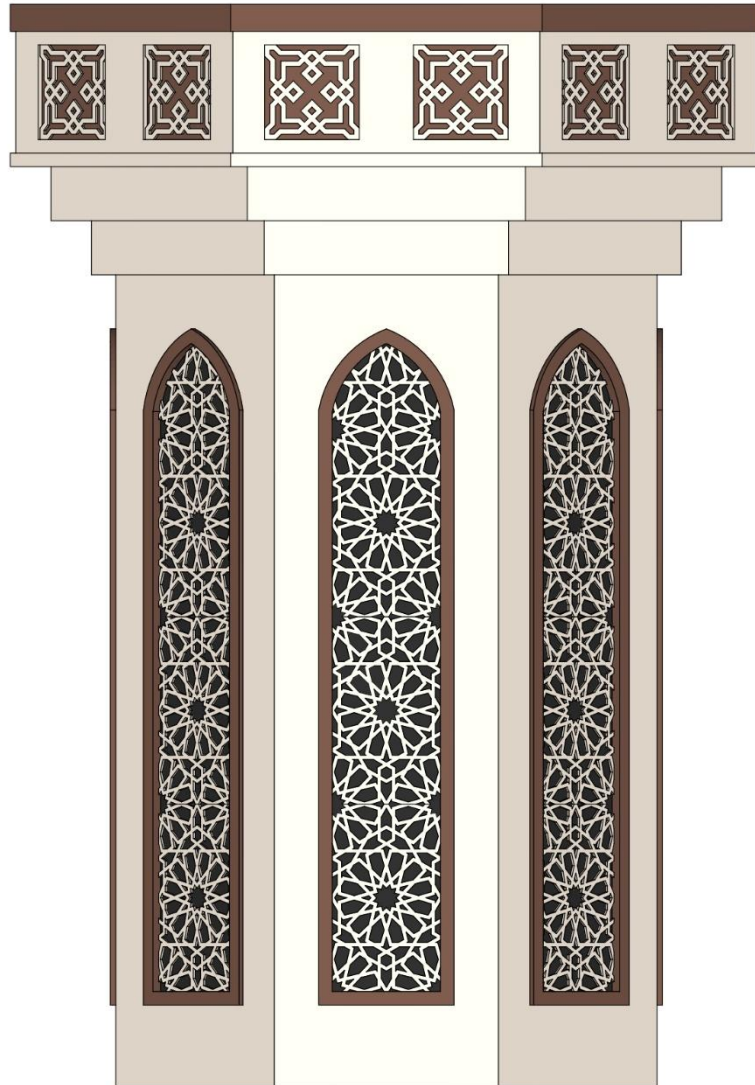

DETAIL ELEVASI 3

Skala 1 : 15


	Nama Proyek	Pemilik Proyek	Nama Gambar	Skala	Digambar Oleh	Ttd	Tanggal
	MENARA MASJID L. 3 T. 23 METER	-	Detail Elevasi 3	1 : 15	GUBUG IMAJINASI 085727292338		30 June 2026
	Lokasi Proyek	Catatan			Disetujui Oleh	Ttd	No Lembar
	-	-					08
							A3

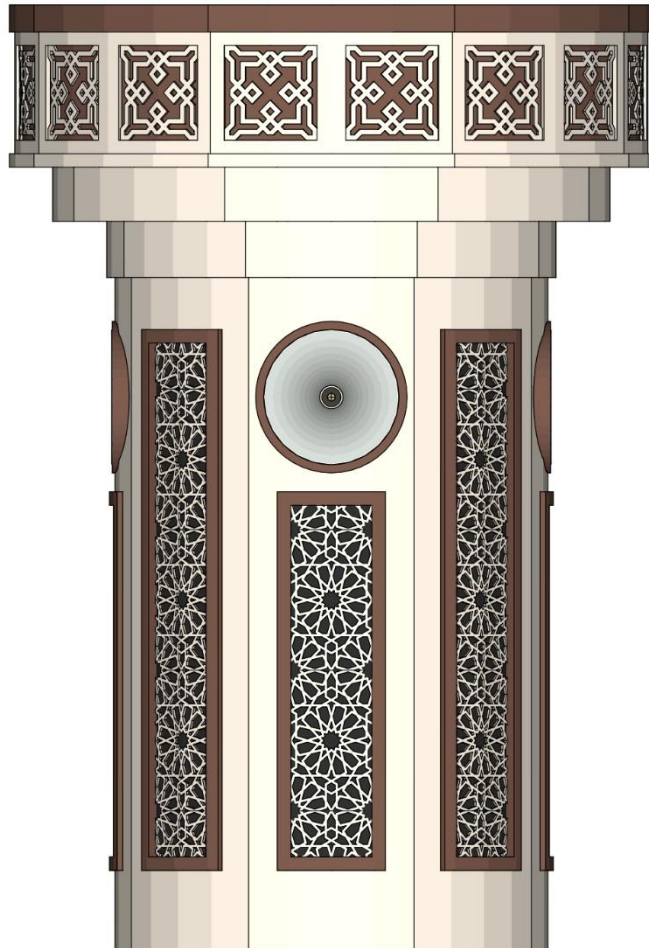

DETAIL ELEVASI 4

Skala 1 : 15


	Nama Proyek	Pemilik Proyek	Nama Gambar	Skala	Digambar Oleh	Ttd	Tanggal
	MENARA MASJID L. 3 T. 23 METER	-	Detail Elevasi 4	1 : 15	GUBUG IMAJINASI 085727292338		30 June 2026
	Lokasi Proyek	Catatan			Disetujui Oleh	Ttd	No Lembar
	-	-					09
							A3

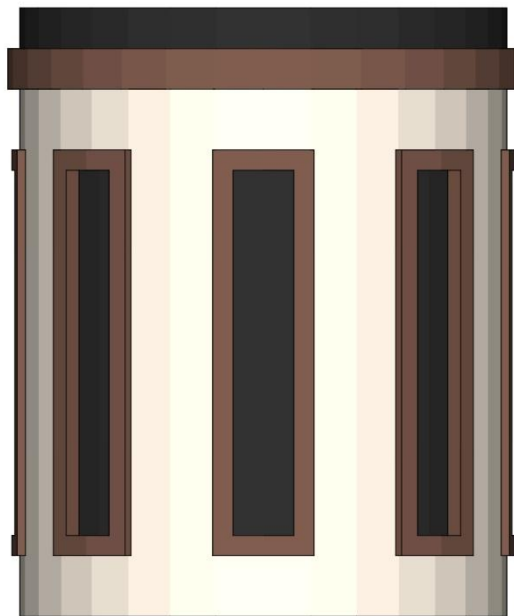

DETAIL ELEVASI 5

Skala 1 : 10

	Nama Proyek	Pemilik Proyek	Nama Gambar	Skala	Digambar Oleh	Ttd	Tanggal
	MENARA MASJID L. 3 T. 23 METER	-	Detail Elevasi 5	1 : 10	GUBUG IMAJINASI 085727292338		30 June 2026
	Lokasi Proyek	Catatan			Disetujui Oleh	Ttd	No Lembar
	-	-					10
							A3

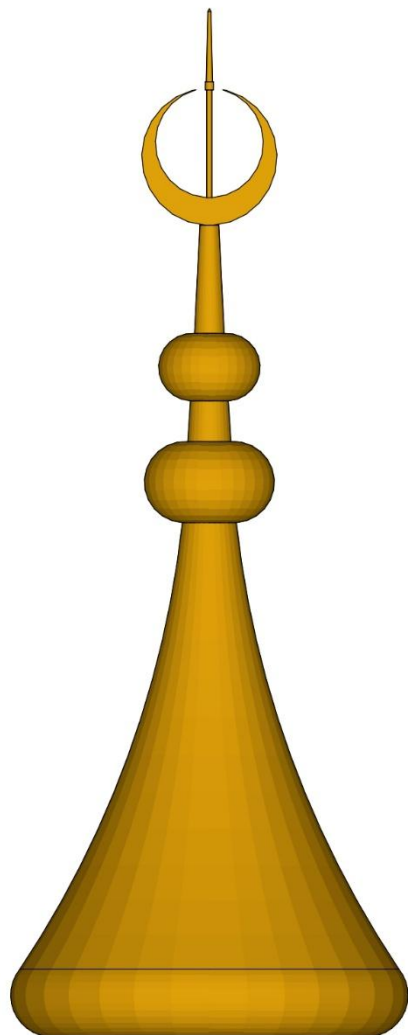

DETAIL MAKARA

Skala 1 : 15

Skala 1 : 15								
	Nama Proyek	Pemilik Proyek	Nama Gambar	Skala	Digambar Oleh	Ttd	Tanggal	
	MENARA MASJID L. 3 T. 23 METER	-	Detail Makara	1 : 15	GUBUG IMAJINASI 085727292338		30 June 2026	
	Lokasi Proyek	Catatan			Disetujui Oleh	Ttd	No Lembar	Ukuran Kertas
	-	-					11	A3